



LONG ROAD — RESIDENCE | LEVEL 1 | ROOM DATA PLAN

EVERY LABEL SITS OUTSIDE THE BUILDING. AREA IN BOTH UNITS, CEILING HEIGHT ON EVERY ROOM. TOTAL 128.90 m² / 1,387.5 SF ACROSS NINE SECTIONS.

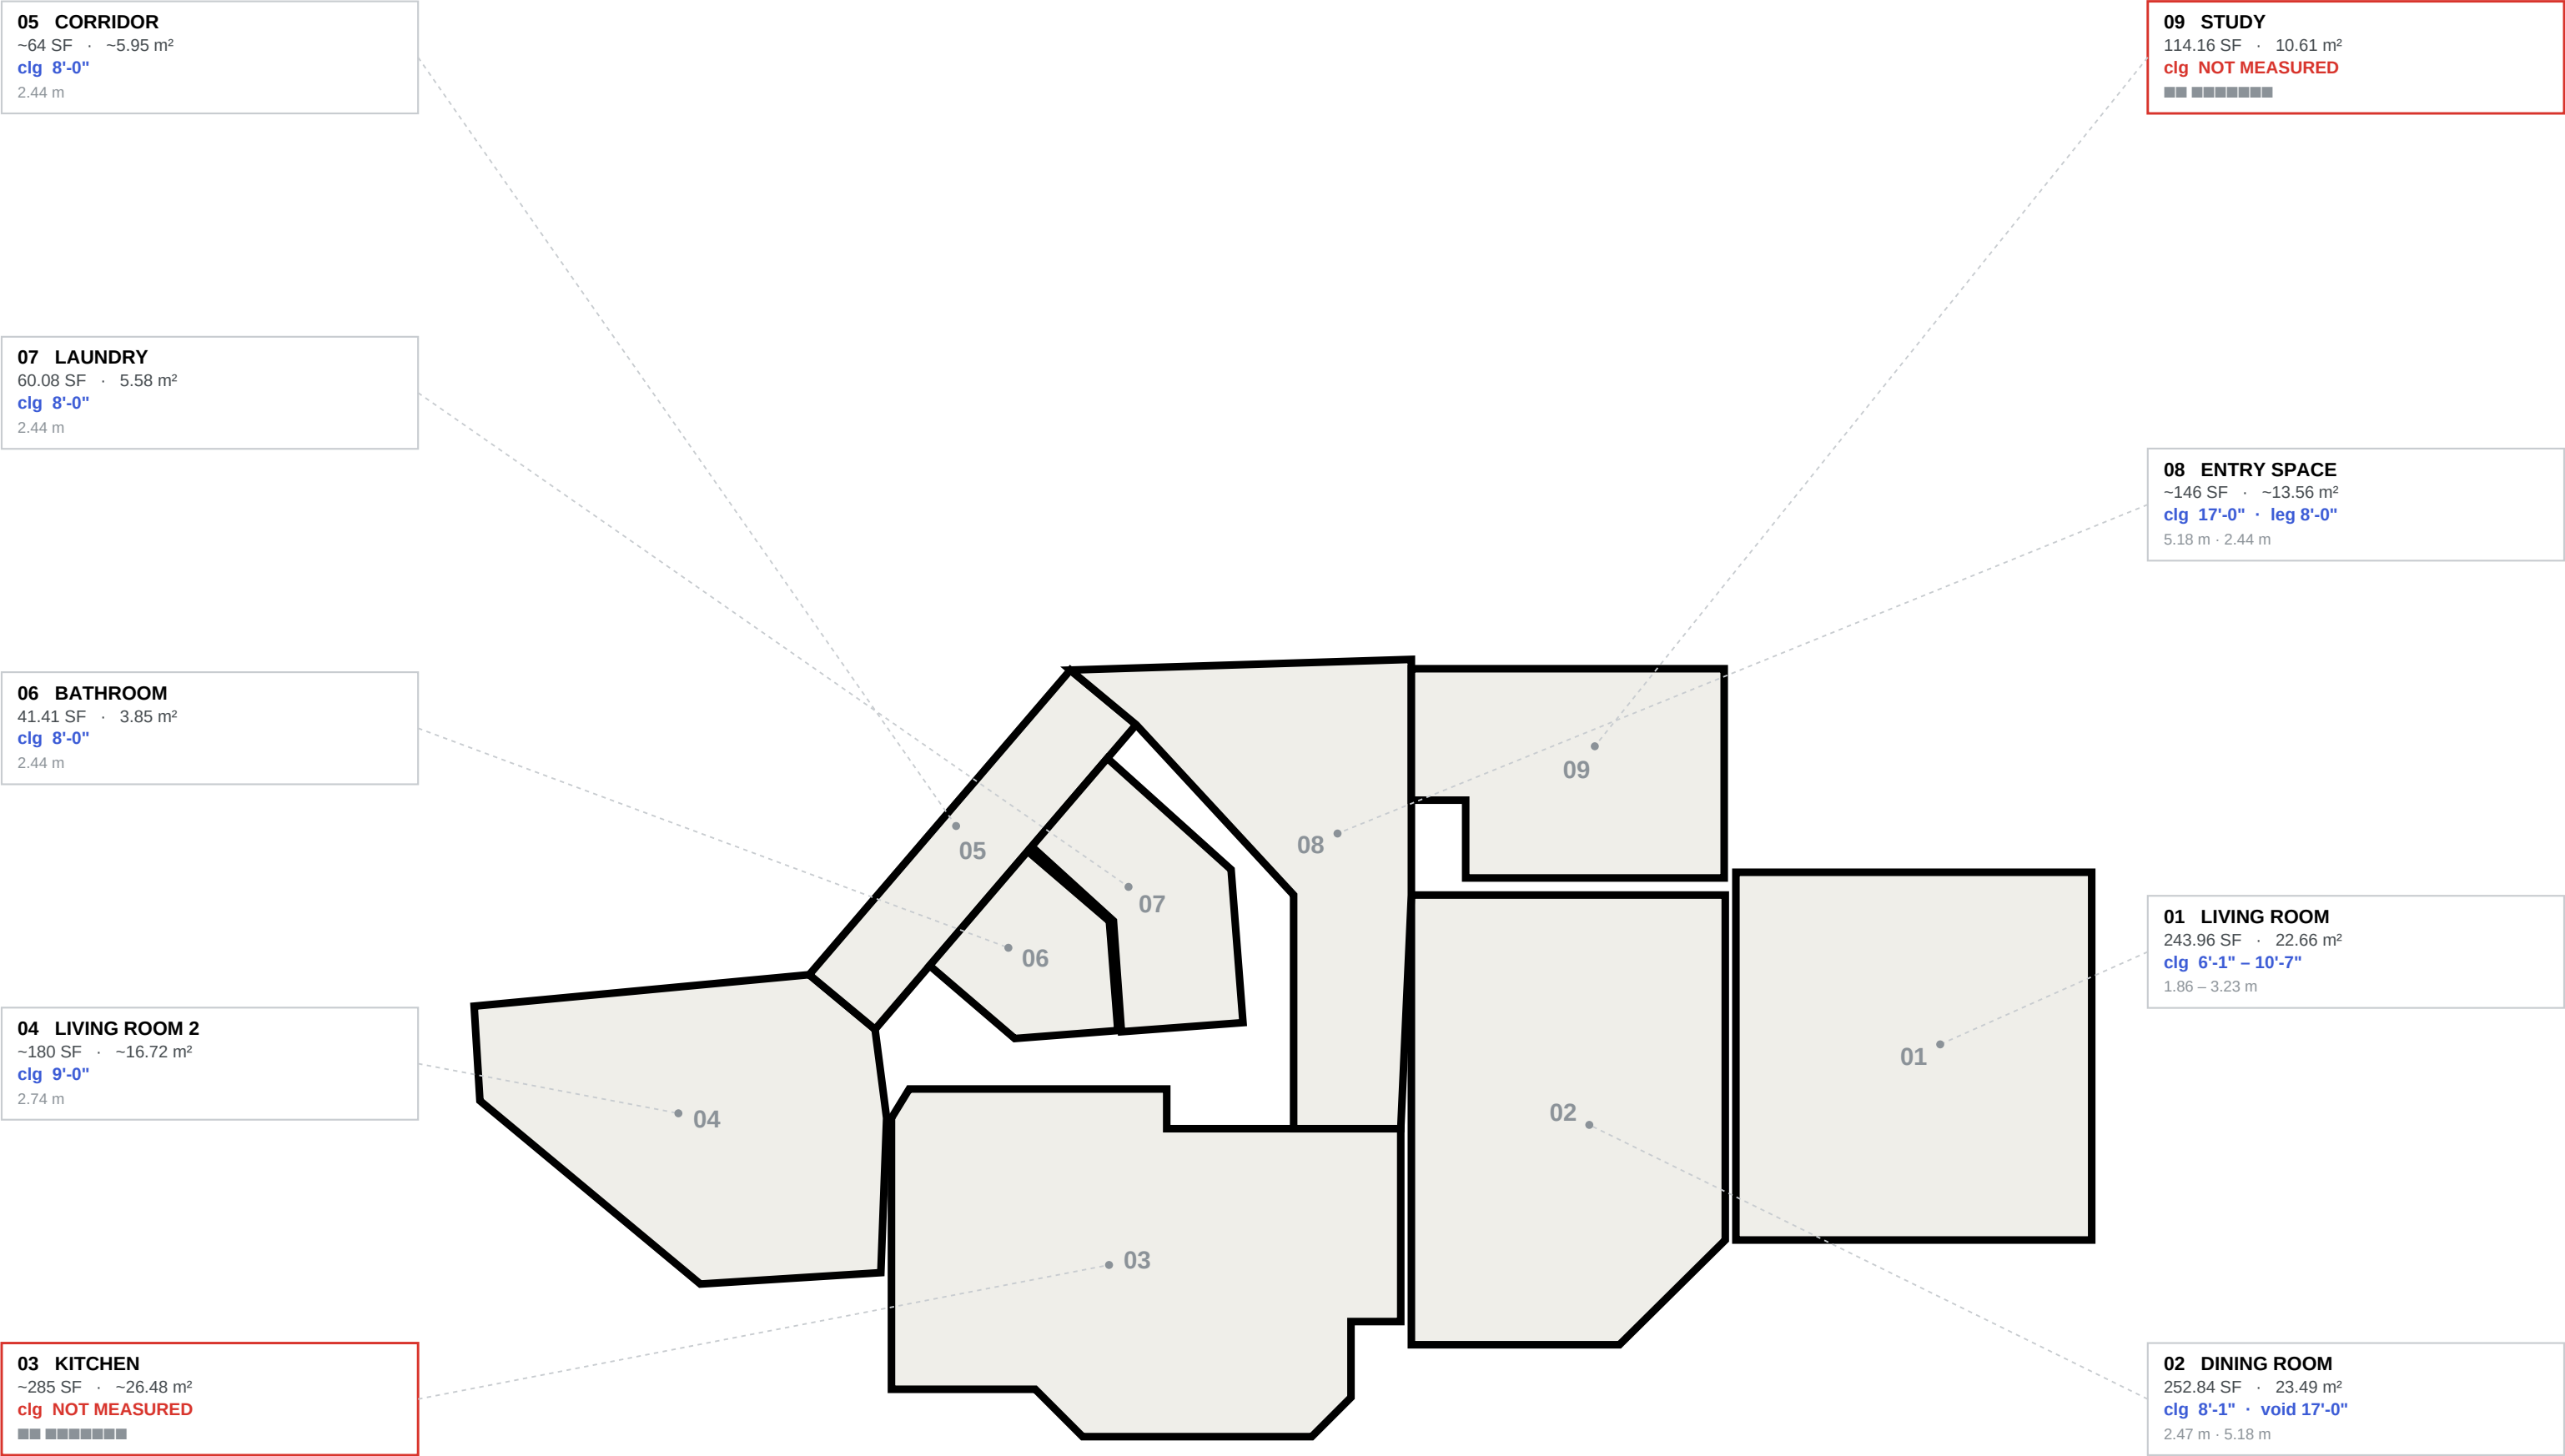

LONG ROAD — RESIDENCE | LEVEL 2 | ROOM DATA PLAN


EVERY LABEL SITS OUTSIDE THE BUILDING. FIVE ROOMS SCANNED — 71.58 m² / 770.46 SF. THE STAIR, THE ATTIC AND THE CORRIDOR ARE OWNER FIGURES ONLY AND ARE DRAWN IN AMBER.

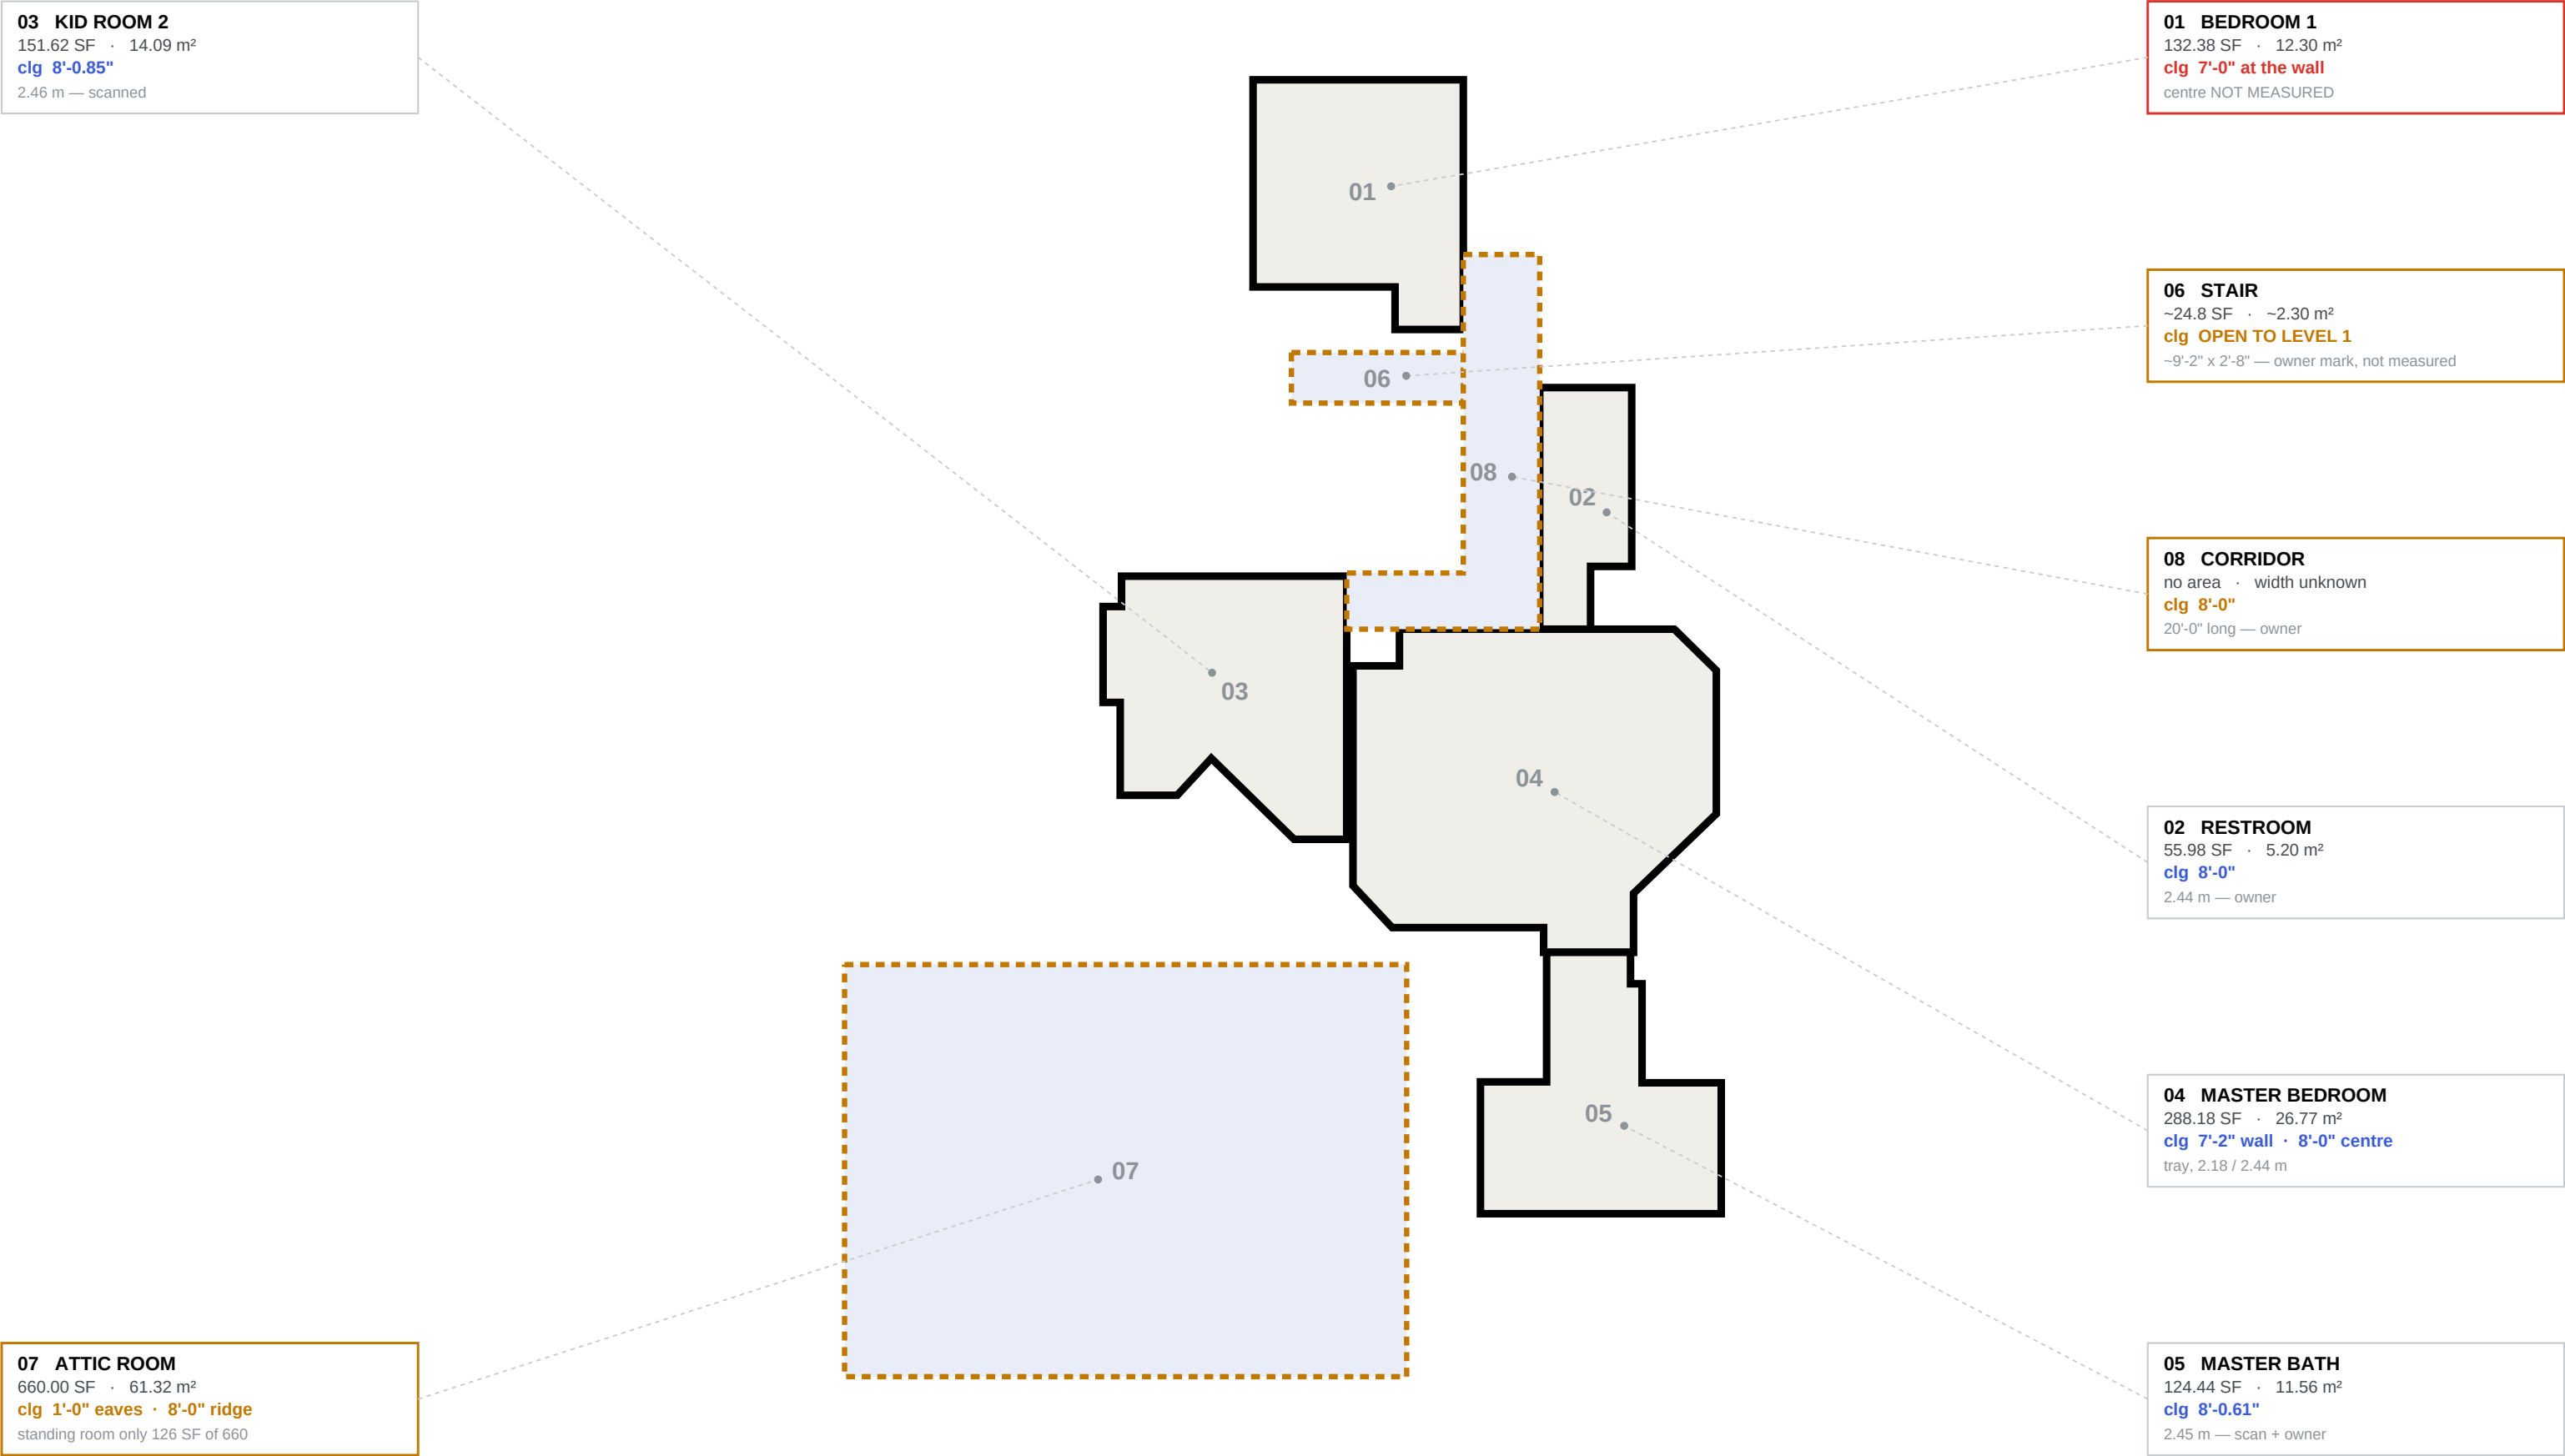

LEVEL 2 — REV. 15 | THE STAIR IS NOT IN THE CORRIDOR — IT IS A SEPARATE ZONE WEST OF IT

THIS RETIRES THE SIXTEEN-FOOT PROBLEM I HAVE FLAGGED SINCE REV. 6. THE CORRIDOR IS CORRIDOR FOR ALL 20 FT; THE STAIR IS ITS OWN ZONE. ALL TWENTY-EIGHT OVERLAP PAIRS ZERO.

1 — LEVEL 2 FLOOR PLAN

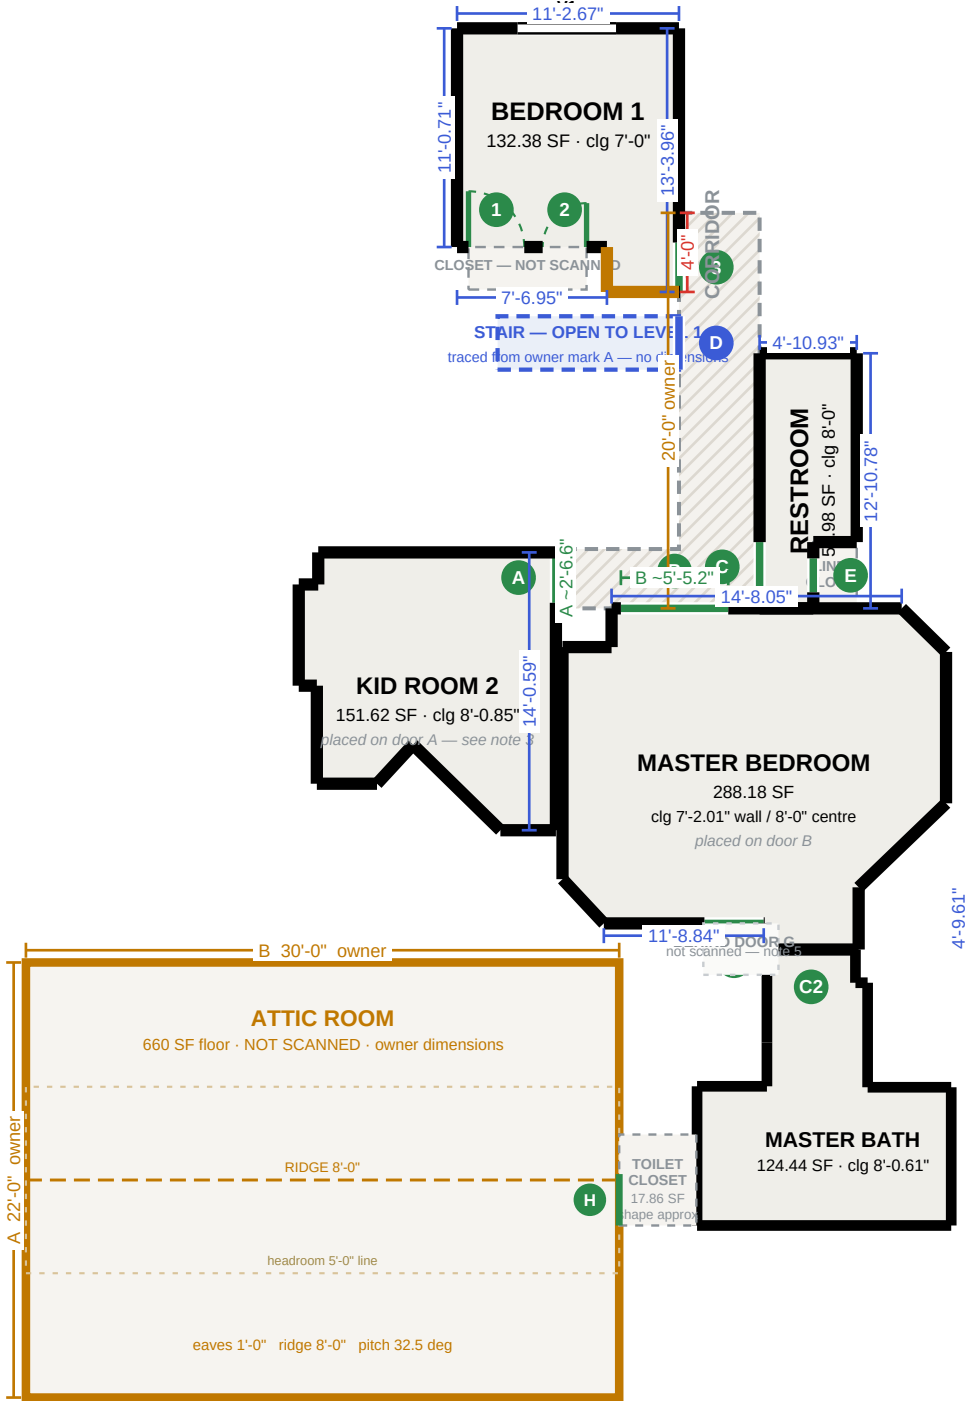

2 — VALIDATION AGAINST THE SCANS' OWN FIGURES

Three of the five scans carry an overview table. Where one exists, my polygon is checked against it. Where none exists, the area has no second source and says so.

SECTION	MY AREA	SCAN AREA	MY PERIM	SCAN PERIM	ANGLE FIX
MASTER BATH	124.45 SF	124.44 SF	53'-7.38"	53'-7.36"	0.00 deg PASS
KID ROOM 2	151.62 SF	151.63 SF	54'-4.61"	54'-4.61"	5.29 deg PASS
MASTER BEDROOM	288.18 SF	288.02 SF	68'-2.20"	68'-2.21"	1.99 deg PASS
BEDROOM 1	132.38 SF	no table	49'-1.26"	no table	0.00 deg unchecked
RESTROOM	55.98 SF	no table	35'-7.42"	no table	0.00 deg unchecked

OVERLAP TEST — ALL TWENTY-EIGHT PAIRS, 0.000000 SF

Eight placed sections, twenty-eight pairs, intersection area zero for every one. The stair zone clears bedroom 1 by 1 ft 2.7 in and kid room 2 by 9 ft 2.9 in.

ATTIC HEADROOM — WHAT 660 SF OF FLOOR ACTUALLY BUYS

Eaves 1'-0", ridge 8'-0", span 22 ft. The roof rises 7 ft over 11 ft — a 32.5 degree pitch.

MEASURE	AREA	SHARE
Floor area	660.0 SF	100%
Where headroom is at least 5'-0"	282.9 SF	43%
Where headroom is at least 6'-8" (standing)	125.7 SF	19%
Where headroom is at least 7'-0"	94.3 SF	14%

Arithmetic from your two heights, not a measurement. The 3 ft line is dashed on the plan.

3 — ROOM DATA

SECTION	AREA	CEILING	CHECKED AGAINST SCAN
01 BEDROOM 1	132.38 SF	7'-0" — centre?	no overview table
02 RESTROOM	55.98 SF	8'-0" owner	no overview table
03 KID ROOM 2	151.62 SF	8'-0.85" scan	PASSED — 151.63 SF
04 MASTER BEDROOM	288.18 SF	7'-2" / 8'-0"	PASSED — 288.02 SF
05 MASTER BATH	124.44 SF	8'-0.61" both	PASSED — 124.44 SF
toilet closet	17.86 SF	8'-0.61" scan	scan, shape approx
06 STAIR	~24.8 SF	open to Level 1	NOT SCANNED — owner mark
07 ATTIC ROOM	660.00 SF	1'-0" to 8'-0"	NOT SCANNED — owner
08 CORRIDOR	not measured	8'-0" owner	20'-0" long, owner
SCANNED TOTAL	770.46 SF	—	5 of 8 sections

4 — OPENING & DOOR SCHEDULE

TAG	CONNECTS	WIDTH	NOTES
1 / 2	BEDROOM 1 - closet	~2'-9.8" / 2'-2.6"	scaled off scan
3	BEDROOM 1 - CORRIDOR	~2'-6"	inside the 4 ft contact
A	KID ROOM 2 - CORRIDOR	~2'-6.6"	in the 14'-0.59" wall — mated
B	CORRIDOR - MASTER BEDROOM	~5'-5.2"	in the 14'-8.05" wall — mated
C	CORRIDOR - RESTROOM	~2'-6"	in the 12'-10.78" wall
D	CORRIDOR - STAIR	unknown	stair is west of the corridor
E	RESTROOM - linen closet	20.63"	in the 3'-4.21" wall
F	KID ROOM 2 - its closet	3'-0.5"	from the scan
C2	MASTER - MASTER BATH	~4'-6"	your red C, in the 4'-9.61" wall — mated
G	MASTER - unknown space	~3'-0"	still has no destination
H	TOILET CLOSET - ATTIC ROOM	unknown	the only way in — owner
V1 / V2	BEDROOM 1 / RESTROOM window	4'-11.82" / 17.48"	from the scans
V3-V5	MASTER windows, bay	3 windows	positions not drawn

5 — CEILING SCHEDULE

A scan reports the height at the wall. In a trayed, vaulted or pitched room that is the LOW figure.

6 — NOTES

- I HAD THE STAIR IN THE WRONG PLACE, AND THAT WAS THE THING THAT NEVER ADDED UP. You marked A as the stair and B as the corridor. I had been treating the lower sixteen feet of the corridor strip AS the stair. It is not in the corridor at all — it is a separate zone WEST of it, immediately south of bedroom 1, and the corridor is corridor for all twenty feet.
- THIS RETIRES A NOTE I HAVE CARRIED SINCE REV. 6. Every revision since has said that twenty feet of corridor minus four against bedroom 1 left about sixteen feet for a stair, when a flight runs ten to thirteen. The arithmetic was never wrong — my placement was. With the stair moved out, the corridor is a plain 20 ft run and nothing is left over. That note is gone.
- THE STAIR ZONE IS TRACED FROM YOUR MARK, NOT MEASURED. Your two red lines put it at roughly 9'-2" by 2'-8", about 25 SF, drawn dashed in blue with no dimensions. One thing worth saying: 2'-8" is narrow. A flight is normally 3'-0" or wider, and 2'-8" is around the minimum clear width for the flight itself, never mind the floor opening. Either the marks are approximate or this is a genuinely tight stair. One tape measurement across it settles it.
- DOOR D MOVES WITH THE STAIR. It is now an opening in the corridor's west wall over the stair's run, so you step west off the corridor onto the flight. Before it opened onto a zone inside the corridor, which was never right.
- WHAT THIS DOES NOT FIX. The stair is still the only physical link between the two floors and it is still unmeasured — run direction, tread count, width, and the size of the opening it makes in the Level 2 floor. Until that exists the two levels cannot be aligned to each other, and the combined file says so on its face.
- NOTHING ELSE MOVED. Bedroom 1, the restroom, kid room 2, the master, the master bath and the attic are all where REV. 14 left them. Overlap test now runs twenty-eight pairs across eight placed sections and every one returns 0.000000 SF. The stair zone clears bedroom 1 by 1'-2.7" and kid room 2 by 9'-2.9".
- FIVE ROOMS ARE SCANNED AND THREE VALIDATE AGAINST THE SCAN'S OWN OVERVIEW TABLE — master bath, kid room 2 and the master bedroom, each reproducing its reported area and perimeter. Bedroom 1 and the restroom have no overview table and so no second source; their areas rest on my arithmetic alone.
- THE MASTER BATH IS THE CLEANEST ROOM ON THIS FLOOR. Eleven right-angle walls, zero angle correction, area 124.45 SF against 124.44, perimeter 53'-7.38" against 53'-7.36". Eleven of its fifteen listed walls sum to exactly the reported total perimeter, which identified the outline before a line was drawn.
- THE TWO WALLS AT DOOR C2 ARE NOT THE SAME LENGTH — master 4'-9.61", bath 4'-5.72", 3.89 in apart. Two scans measuring one partition from opposite rooms. Shorter centred on longer, neither changed, neither averaged. The toilet closet is dashed at 17.86 SF, shape approximate.
- THE ATTIC IS NOT A MEASUREMENT. 30 by 22 ft, eaves 1 ft, ridge 8 ft, entered from the toilet closet — your figures, in amber, excluded from the scanned total. 660 SF of floor is not 660 SF of room: at a 32.5 degree pitch you can stand up in a band 4'-2" wide, 126 SF, 19 per cent. Which way the ridge runs is an assumption.
- BEDROOM 1 IS THE ONLY OPEN CEILING. 7'-0" at the wall, centre never measured, same sloped soffit in the photos as the master's tray. Your master bath figure of 8 ft against the scan's 8'-0.61" is still the only direct evidence the typed ceilings are sound.
- DOOR G STILL HAS NO DESTINATION. The master scan counts two doors, B and G; C2 is a third opening in a different wall, so G is not the bath. Photo 8 looks from the bath at the master's dresser through a doorway.
- The corridor still has one owner-stated length and a guessed width, and every section except bedroom 1 is positioned by a chain of mated doors that starts there.
- REV. 1 through 14 are superseded. Level 1 sheets A-10 and A-10M are unaffected.

7 — NEXT

- STAIR — width across the flight, run direction, tread count, and the opening in the Level 2 floor. This is now the only thing between two correct floors and one correct house.
- CORRIDOR — one width measurement across it.
- BEDROOM 1 — is its ceiling a tray? One reading in the middle. DOOR G — where does it go?

LONG ROAD — RESIDENCE | LEVEL 2 OF 2


SOURCE: Doc 16, 18, 19, 20, 21 scans Aug 6 + 28 photos, owner sketch, mark-ups, ceilings, corridor and attic figures
SECTIONS: 8 SCANNED: 5 PLACED: 8 SUPERSEDES REV. 1 THROUGH 14

SHEET A-20 / LEVEL 2 — IMPERIAL REV. 15 — AUG 2026


LEVEL 1 — NINE SECTIONS | ALL SCANNED ROOMS PLACED

SHELL ONLY — NO WINDOWS SHOWN. ALL DIMENSIONS IN METRES.

1 — COMBINED FLOOR PLAN (LEVEL 1)

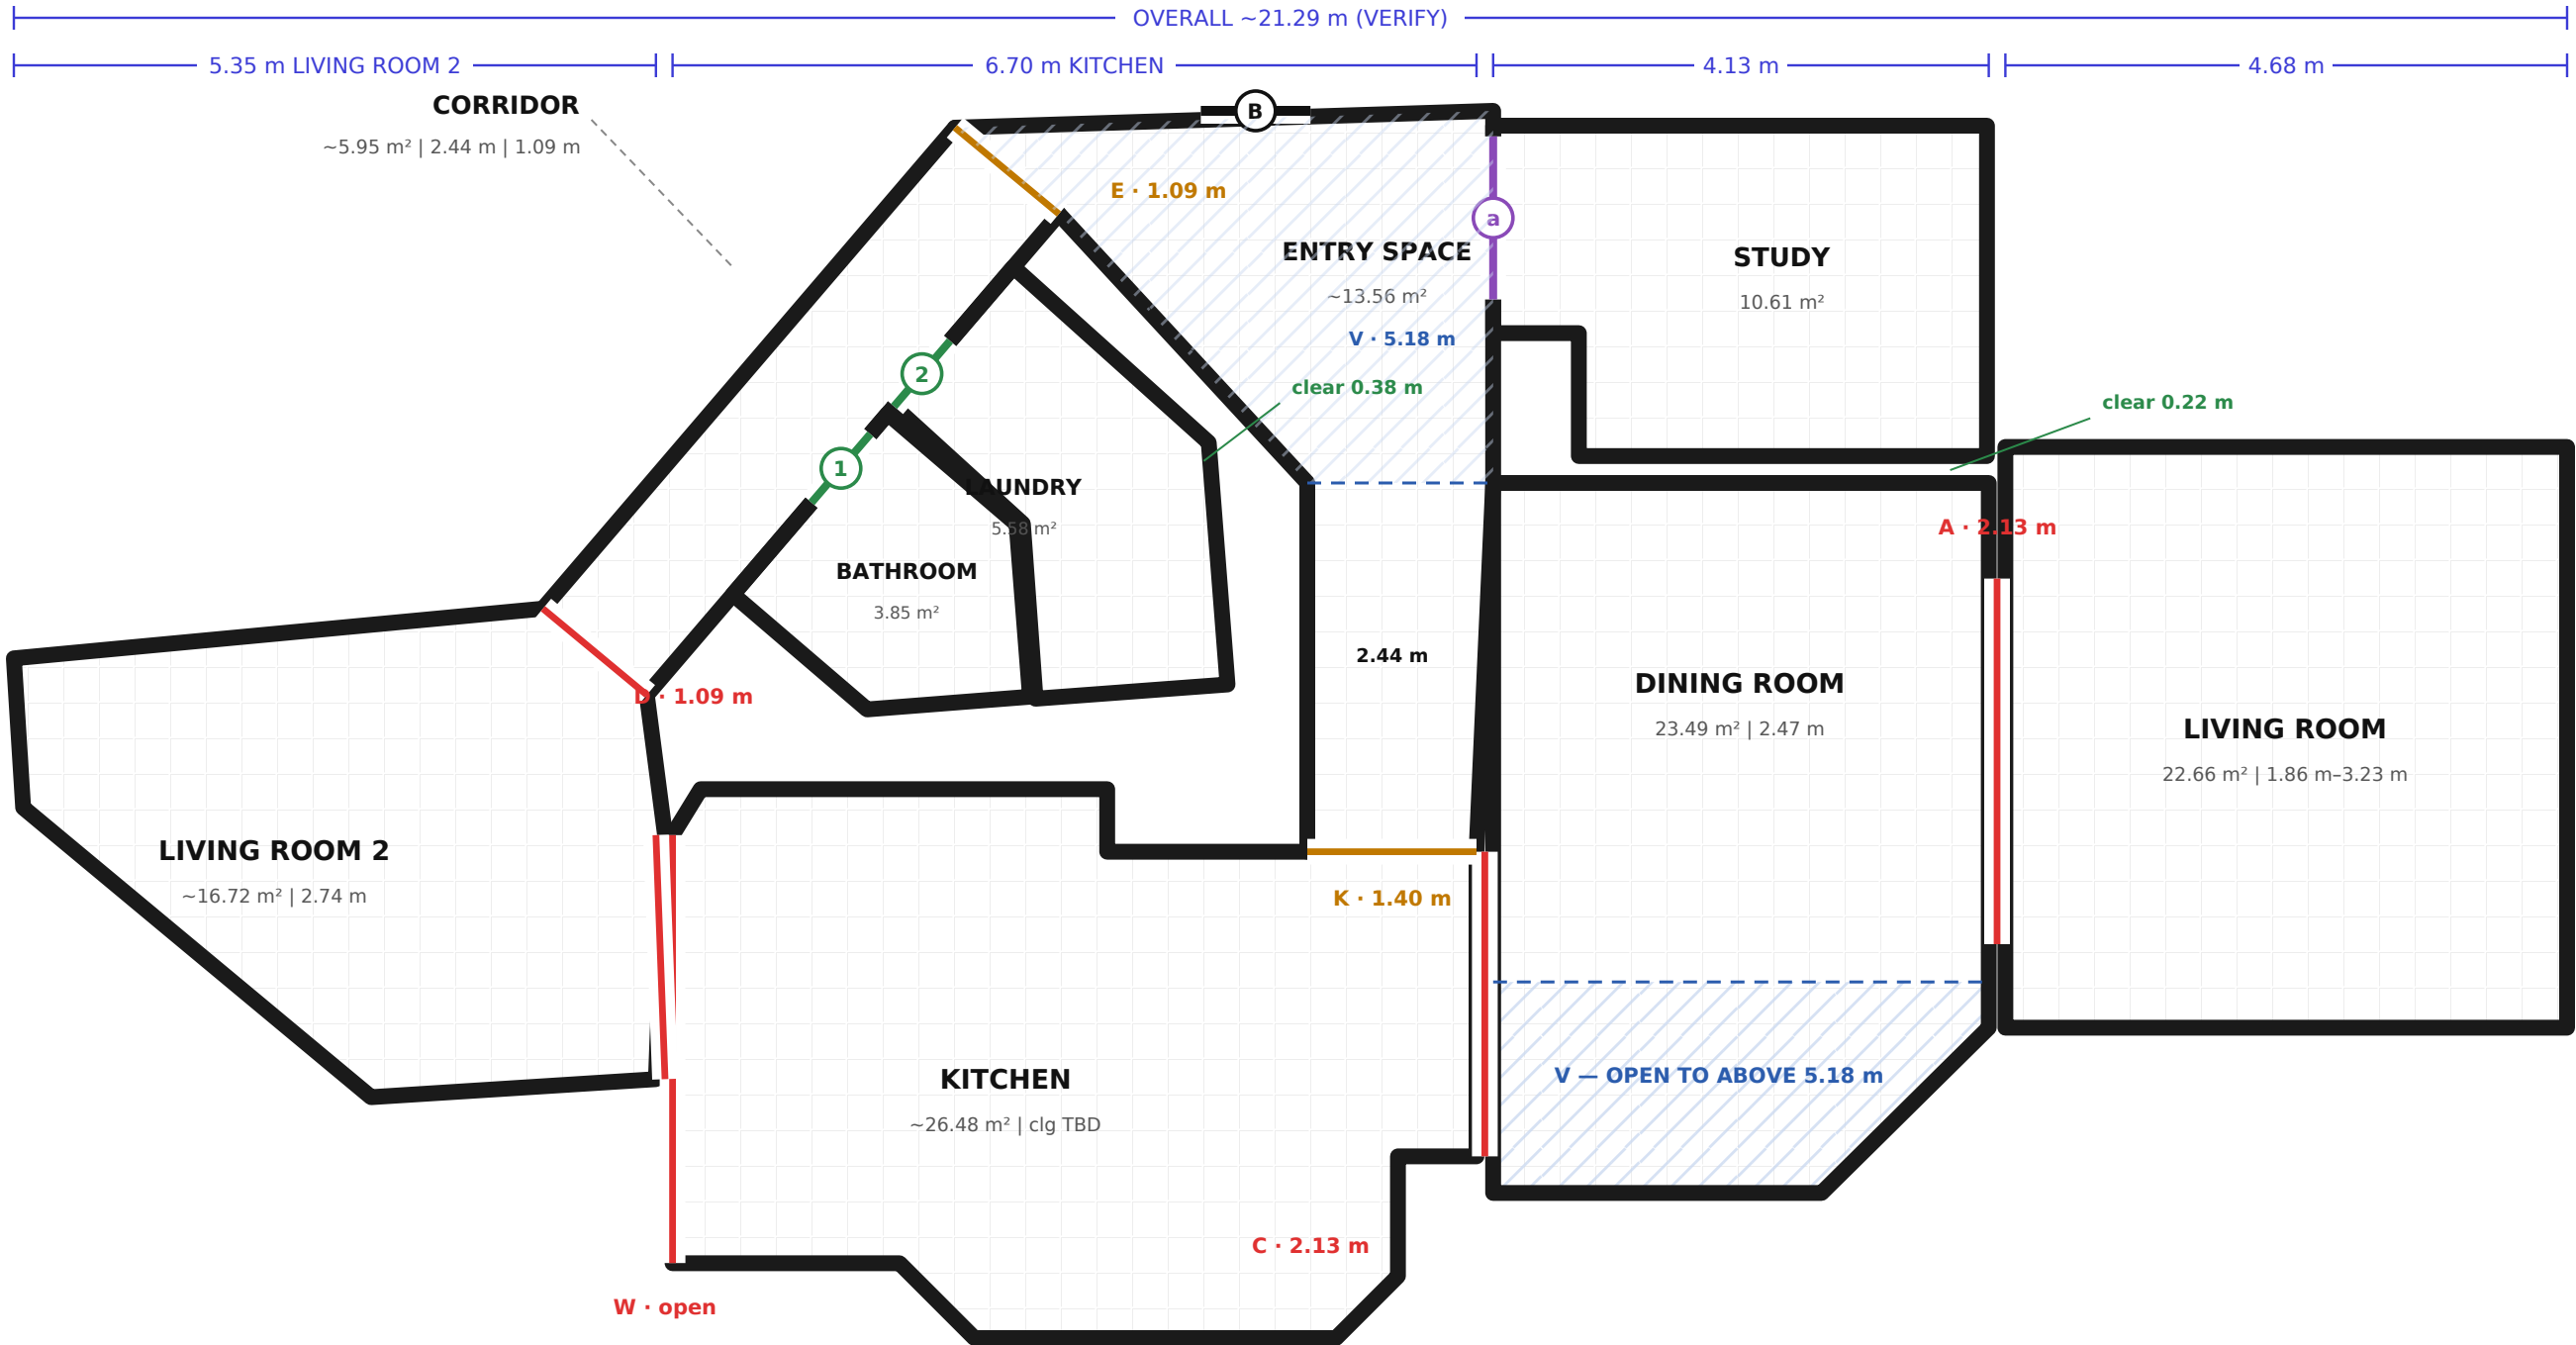

2 — CIRCULATION DIAGRAM (TOPOLOGY, NOT TO SCALE)

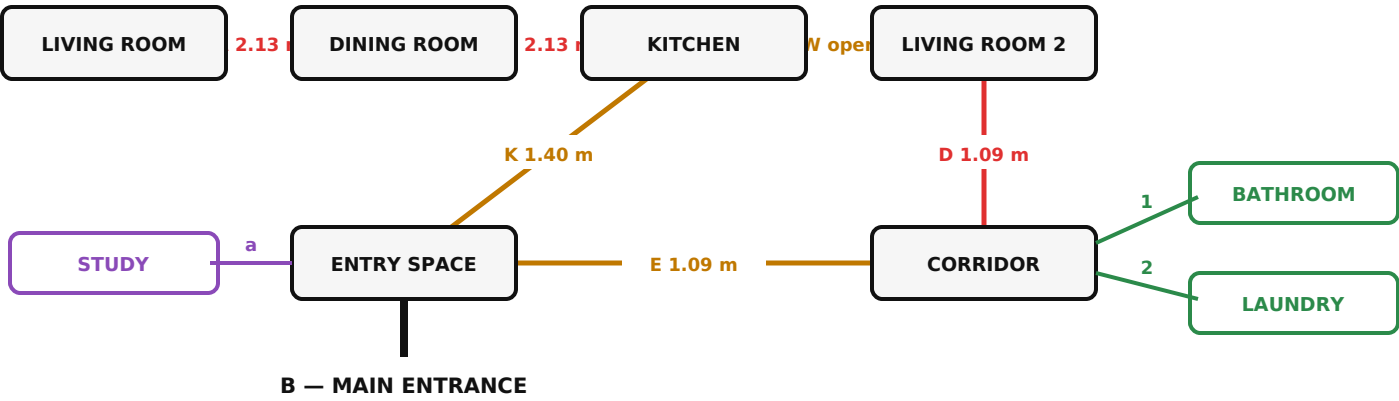

Six rooms form the closed loop; bathroom, laundry and study hang off it as dead ends.

- NOTES:**
- Study outline closes on its own arithmetic: right wall 3.40 m + notch 0.71 m = left wall 4.12 m, and bottom 1.73 m + notch 1.02 m = top 2.75 m. No angle correction needed — this room is exact. Area 10.61 m².
 - Opening W (kitchen ↔ Living 2) is the last unresolved item on Level 1: 3.57 m on the kitchen side vs 2.03 m on the Living 2 side. Everything else closes. Measure W and the drawing is finished.
 - Zero overlap between any two rooms. Study clears the dining room by 0.22 m; entry space clears the laundry by 0.38 m.
 - Door a reads about 1.35 m wide from the study scan — a wide cased opening rather than a normal door. That scan is internally ambiguous (leaf and swing arc disagree), so confirm the width and whether it is a door or an open case.
 - Ceiling heights still missing for kitchen and study only. Bathroom and laundry sit only 0.04 m apart — likely a shared partition.
 - Main door B position along the entry wall is placed by eye from the owner mark-up. No windows drawn anywhere.
 - Metric conversion of sheet A-10. Source measurements were taken in feet and inches; values here are converted, not re-measured.

3 — ROOM DATA

SECTION	AREA	CEILING	SOURCE
LIVING ROOM	22.66 m²	1.86 m – 3.23 m	File 5
DINING ROOM	23.49 m²	2.47 m / 5.18 m	File 6
KITCHEN	~26.48 m²	TBD — measure	File 7
LIVING ROOM 2	~16.72 m²	2.74 m	File 8
CORRIDOR	~5.95 m²	2.44 m	File 9
BATHROOM	3.85 m²	2.44 m	File 11
LAUNDRY	5.58 m²	2.44 m	File 10
ENTRY SPACE	~13.56 m²	5.18 m / 2.44 m	owner mark-up
STUDY	10.61 m²	TBD — measure	File 12
TOTAL — 9 SECTIONS	~128.9 m²	—	


4 — OPENING & DOOR SCHEDULE

TAG	CONNECTS	WIDTH	HEAD	NOTES
A	DINING ROOM ↔ LIVING ROOM	~3.05 m	2.13 m	open
C	DINING ROOM ↔ KITCHEN	2.54 m	2.13 m	open
W	KITCHEN ↔ LIVING ROOM 2	3.57 m / 2.03 m	TBD	see note 2
D	LIVING ROOM 2 ↔ CORRIDOR	1.09 m	TBD	open
E	CORRIDOR ↔ ENTRY SPACE	1.09 m	TBD	open
K	ENTRY SPACE ↔ KITCHEN	~1.40 m	TBD	open
1	CORRIDOR → BATHROOM	0.75 m	TBD	door
2	CORRIDOR → LAUNDRY	0.72 m	TBD	door
B	MAIN ENTRANCE	~0.91 m	TBD	see note 6
a	ENTRY SPACE → STUDY	~1.35 m	TBD	see note 4


УРОВЕНЬ 1 — ДЕВЯТЬ СЕКЦИЙ | ВСЕ ОТСКАНИРОВАННЫЕ ПОМЕЩЕНИЯ РАЗМЕЩЕНЫ

ТОЛЬКО КОРОБКА — ОКНА НЕ ПОКАЗАНЫ. ВСЕ РАЗМЕРЫ В МЕТРАХ.

1 — СОВМЕЩЁННЫЙ ПЛАН ЭТАЖА (УРОВЕНЬ 1)

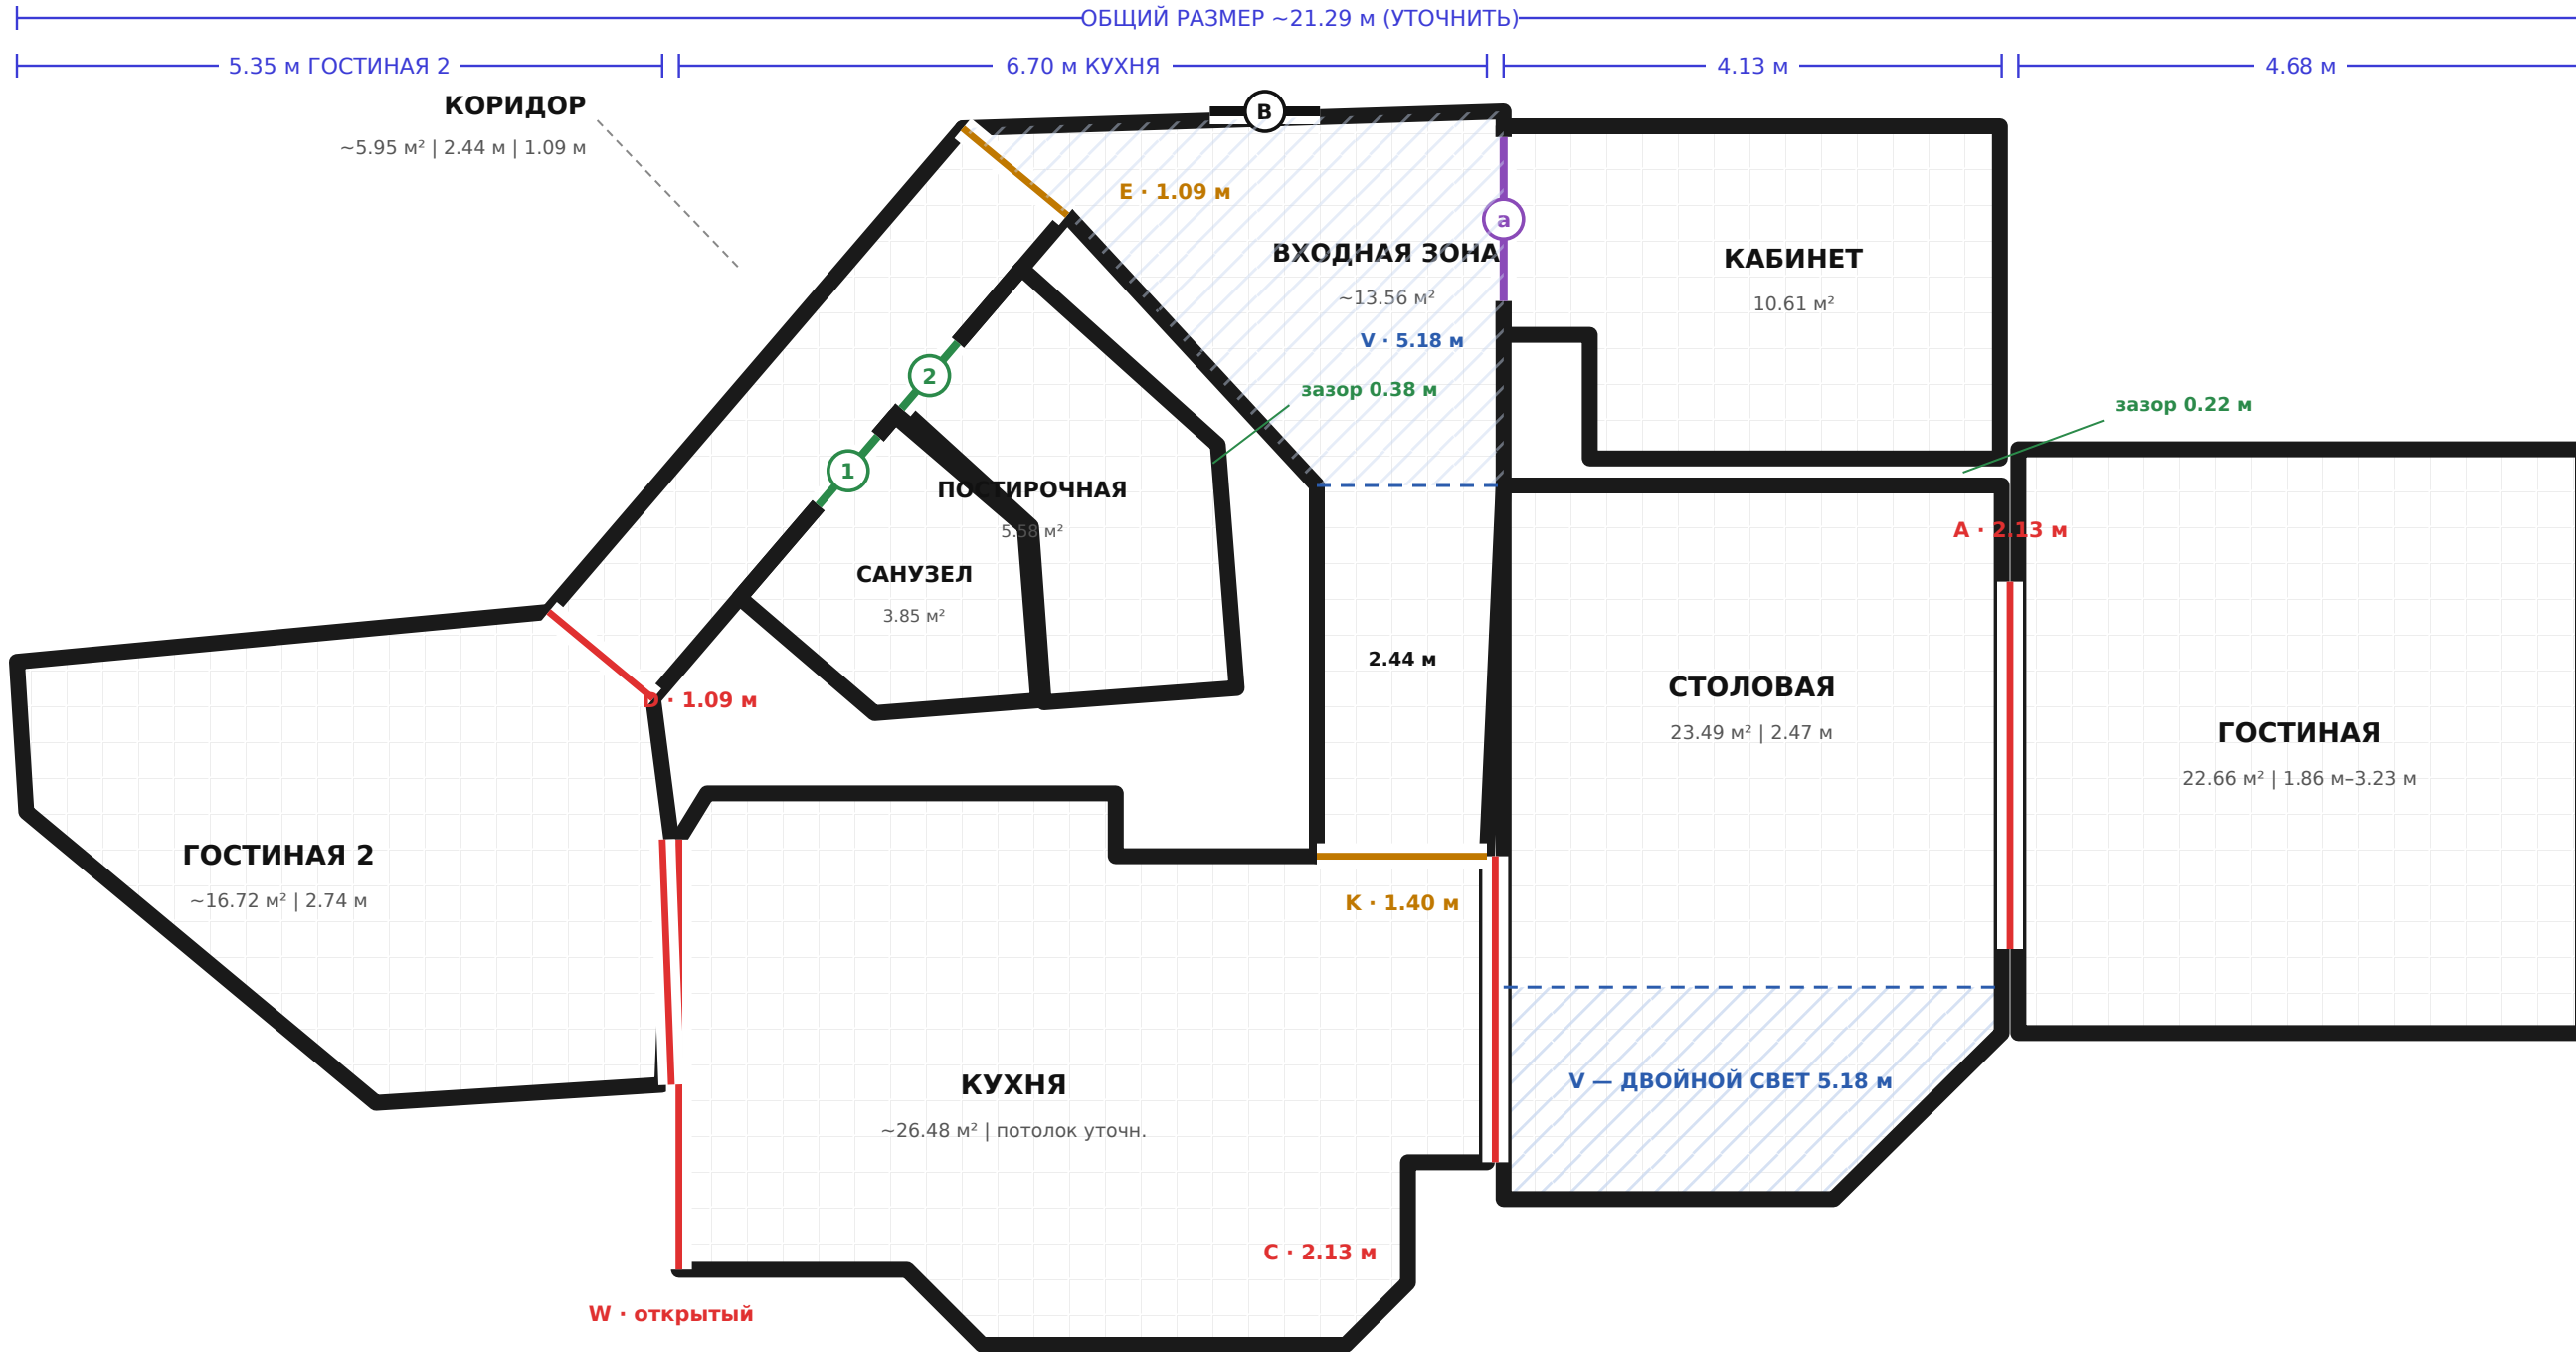

2 — СХЕМА СВЯЗЕЙ (ТОПОЛОГИЯ, НЕ В МАСШТАБЕ)

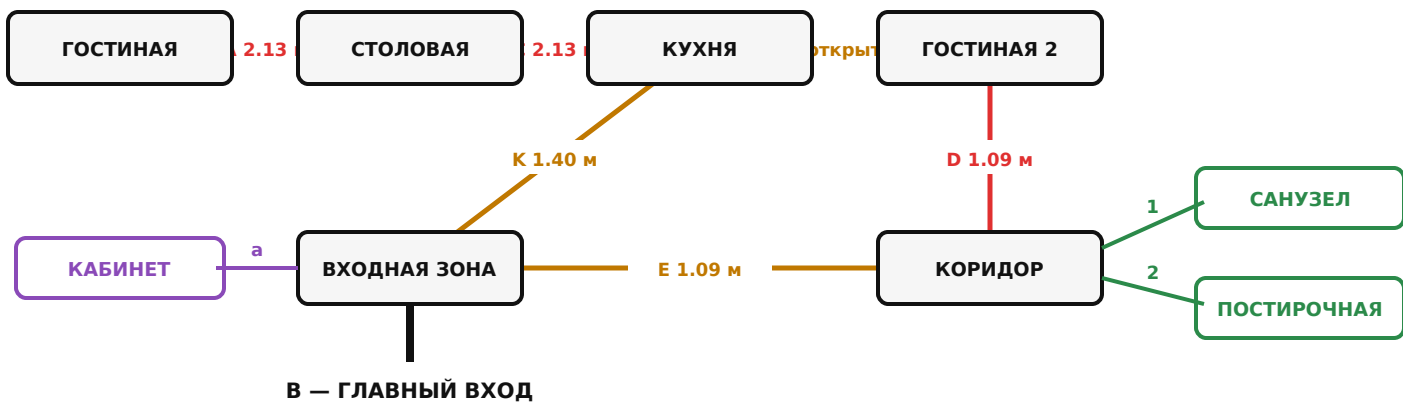

Шесть помещений образуют замкнутое кольцо; санузел, постирочная и кабинет — тупиковые ответвления.

ПРИМЕЧАНИЯ:

- Контур кабинета сходится по собственной арифметике: правая стена 3.40 м + вырез 0.71 м = левая стена 4.12 м, и низ 1.73 м + вырез 1.02 м = верх 2.75 м. Углы подгонять не пришлось — помещение точное. Площадь 10.61 м².
- Проём W (кухня ↔ гостиная 2) — единственное нерешённое место на уровне 1: 3.57 м со стороны кухни против 2.03 м со стороны гостиной 2. Всё остальное сходится. Померьте W — и чертёж закончен.
- Пересечений между помещениями нет. Кабинет отстоит от столовой на 0.22 м; входная зона от постирочной на 0.38 м.
- Дверь а по скану кабинета читается как ~1.35 м — это широкий портал, а не обычная дверь. Сам скан там противоречив (полотно и дуга открывания не совпадают), поэтому уточните ширину и есть ли там дверь вообще.
- Высоты потолков не сняты только у кухни и кабинета. Санузел и постирочная стоят в 0.04 м друг от друга — вероятно, общая перегородка.
- Положение входной двери В вдоль стены поставлено на глаз по разметке владельца. Окна нигде не показаны.
- Метрическая версия листа А-10. Исходные замеры сделаны в футах и дюймах; значения здесь пересчитаны, а не переизмерены.

3 — ДАННЫЕ ПО ПОМЕЩЕНИЯМ

ПОМЕЩЕНИЕ	ПЛОЩАДЬ	ПОТОЛОК	ИСТОЧНИК
ГОСТИНАЯ	22.66 м²	1.86 м – 3.23 м	File 5
СТОЛОВАЯ	23.49 м²	2.47 м / 5.18 м	File 6
КУХНЯ	~26.48 м²	уточнить	File 7
ГОСТИНАЯ 2	~16.72 м²	2.74 м	File 8
КОРИДОР	~5.95 м²	2.44 м	File 9
САМУЗЕЛ	3.85 м²	2.44 м	File 11
ПОСТИРОЧНАЯ	5.58 м²	2.44 м	File 10
ВХОДНАЯ ЗОНА	~13.56 м²	5.18 м / 2.44 м	разметка владельца
КАБИНЕТ	10.61 м²	уточнить	File 12
ИТОГО — 9 СЕКЦИЙ	~128.9 м²	—	

4 — ВЕДОМОСТЬ ПРОЁМОВ И ДВЕРЕЙ

ТЕГ	СОЕДИНЯЕТ	ШИРИНА	ВЫСОТА	ПРИМЕЧАНИЯ
А	СТОЛОВАЯ ↔ ГОСТИНАЯ	~3.05 м	2.13 м	открытый
С	СТОЛОВАЯ ↔ КУХНЯ	2.54 м	2.13 м	открытый
W	КУХНЯ ↔ ГОСТИНАЯ 2	3.57 м / 2.03 м	уточн.	см. прим. 2
D	ГОСТИНАЯ 2 ↔ КОРИДОР	1.09 м	уточн.	открытый
E	КОРИДОР ↔ ВХОДНАЯ ЗОНА	1.09 м	уточн.	открытый
K	ВХОДНАЯ ЗОНА ↔ КУХНЯ	~1.40 м	уточн.	открытый
1	КОРИДОР → САМУЗЕЛ	0.75 м	уточн.	дверь
2	КОРИДОР → ПОСТИРОЧНАЯ	0.72 м	уточн.	дверь
В	ГЛАВНЫЙ ВХОД	~0.91 м	уточн.	см. прим. 6
а	ВХОДНАЯ ЗОНА → КАБИНЕТ	~1.35 м	уточн.	см. прим. 4